



LAHORE供水与污水管理项目 - 从LARECHS COLONY至GULSHAN-E-RAVI的污水系统, LAHORE (采用非开挖技术) LAHORE污水与排水项目



项目名称

从LARECHS Colony到Gulshan-e-Ravi的污水系统, Lahore (采用非开挖技术)

部门名称/行业

住房、城市发展与公共卫生工程部 / 水与卫生管理局。

资助机构

亚洲基础设施投资银行 (AIIB)

位置

从LARECHS Colony和Gurumangat Road到Gulshan-e-Ravi, Lahore的干管与支管污水管线敷设。

项目范围

- 通过MTBM敷设主干污水管：
 - Line A: LARECHs Colony至Qartaba Chowk, Lahore (含管道直径1050、1500及2400mm)。长度 = 12.14km。
 - Line B: Gurumangat至Qartaba Chowk, Lahore (含管道直径1050、1500、2400mm)。长度 = 12.82km。
 - Line C: Qartaba Chowk至Gulshan-e-Ravi, Lahore (含管道直径1050及3500mm)。长度 = 7.25km。
- 通过开挖方式铺设450mm横向污水管。长度 = 159m
- 总路线长度 = 32.37km
- 建设最终处理能力为848立方英尺/秒的最终处置站。
- 修复现有排水沟和收集渠道。
- 敷设接户排水管 (450、600和750mm) = 约8.48km。

批准的项目成本

14,165百万PKR

服务人口和面积

2.35百万和15,658英亩 (约)

项目描述

微型隧道掘进机 (MTBM)

- 主干污水管和部分支管将采用微型隧道掘进机 (MTBM) 在地下敷设。
- 将使用以下直径的MTBM, 用于所述长度:

#	管道直径 (毫米)	长度 (公里)
1	1050	9.837
2	1500	5.454
3	2400	11.582
4	3500	5.337
合计		32.210

顶管坑和接收坑的数量 = 165 (约)

不同管径的顶进坑与接收坑的最大间距:

#	管道直径 (毫米)	最大间距 (米)
1	1050	190
2	1500	250
3	2400	350
4	3500	500

开槽

- 支管与骑管污水管将按以下详情采用开挖法敷设:


#	污水管	管道直径 (毫米)	长度 (公里)
1	支管	450	0.159
2	骑管式下水道	450, 600, 750	8.48

微型隧道施工工艺的主要组成部分

微型隧道的

主要组成部分包括:

- 微型隧道掘进机/设备
- 始发井和接收井
- 龙门架/起重机
- 泥浆装载装置
- 发电机
- MTBM承包商单元
- RCC配HDPE衬砌管 (6000 psi强度)
- 自卸卡车

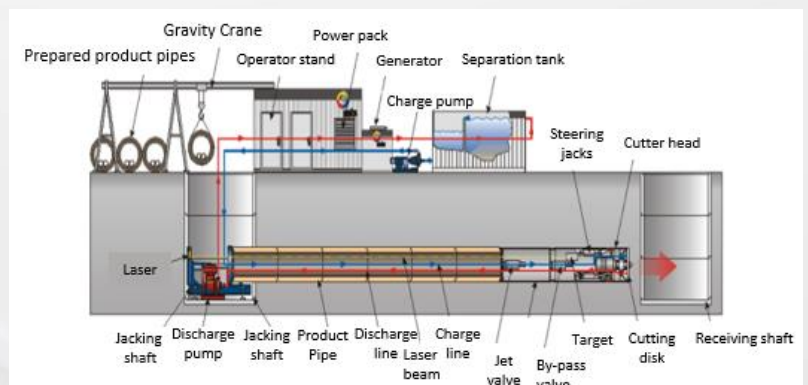

竣工时间

- 设计阶段一 = 6个月
- 执行阶段二 = 30个月

执行模式

工程、采购和施工
(EPC) 模式 - 设计与建造

预期成果

- 通过铺设新的主干污水管道改善现有污水系统，位于 Central Lahore.
- 污水/雨水的安全处置从项目区域。
- 环境改善方面
雨水渠道的恢复与整治
可供利用的
用于城市内休闲活动。

设计阶段一的任务

交付成果

1可行性研究报告

2更新版初步工程设计报告

3更新版岩土工程报告

4更新版地形测量


5更新版ESIA、LRP、RAP、GAP、SEP

6最终招标文件

7招标评估报告

8工程授标

主干污水管敷设位置

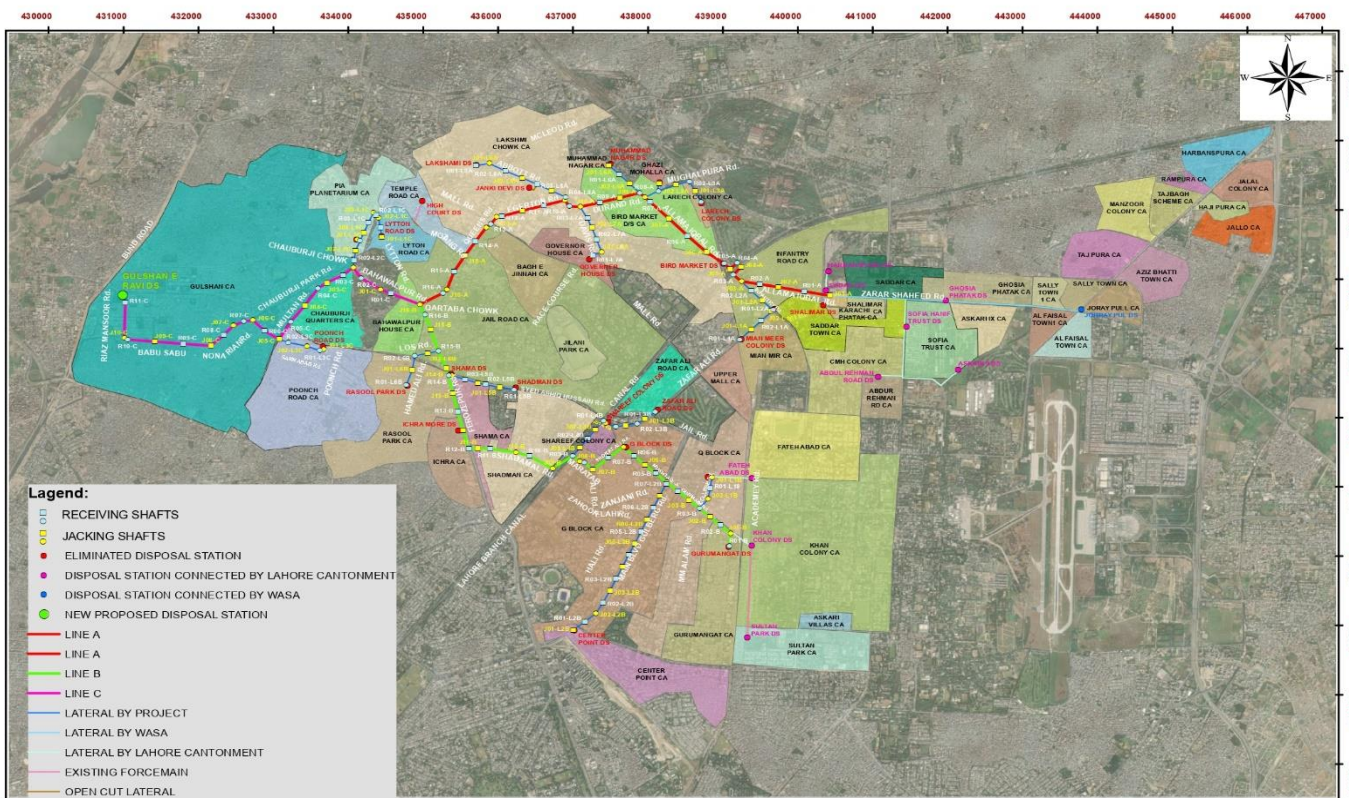

LAHORE WATER & WASTE WATER MANAGEMENT PROJECT-SEWERAGE SYSTEM FROM LARECH COLONY TO GULSHAN-E-RABI, LAHORE (THOUGH TRENCHLESS TECHNOLOGY)															
 WASA LAHORE	WATER AND SANITATION AGENCY, LAHORE	 EBA Engineering & Building Associates	 ISF Infrastructure Services Firm	 CFC Construction & Fabrication Company	 team A Joint Venture	REVISION	04								
							03								
							02								
							01								
						REV.	DATE	DESCRIPTION							
						CONTROL	DRAWN	CHECKED BY	RECOMMENDED	CATCHMENT AREA MAP				SCALE 1:50,000	
							CHO/NER			DATE:	OCT 2024	DRAWING No.	FIGURE	REV:-	
							APPROVED								